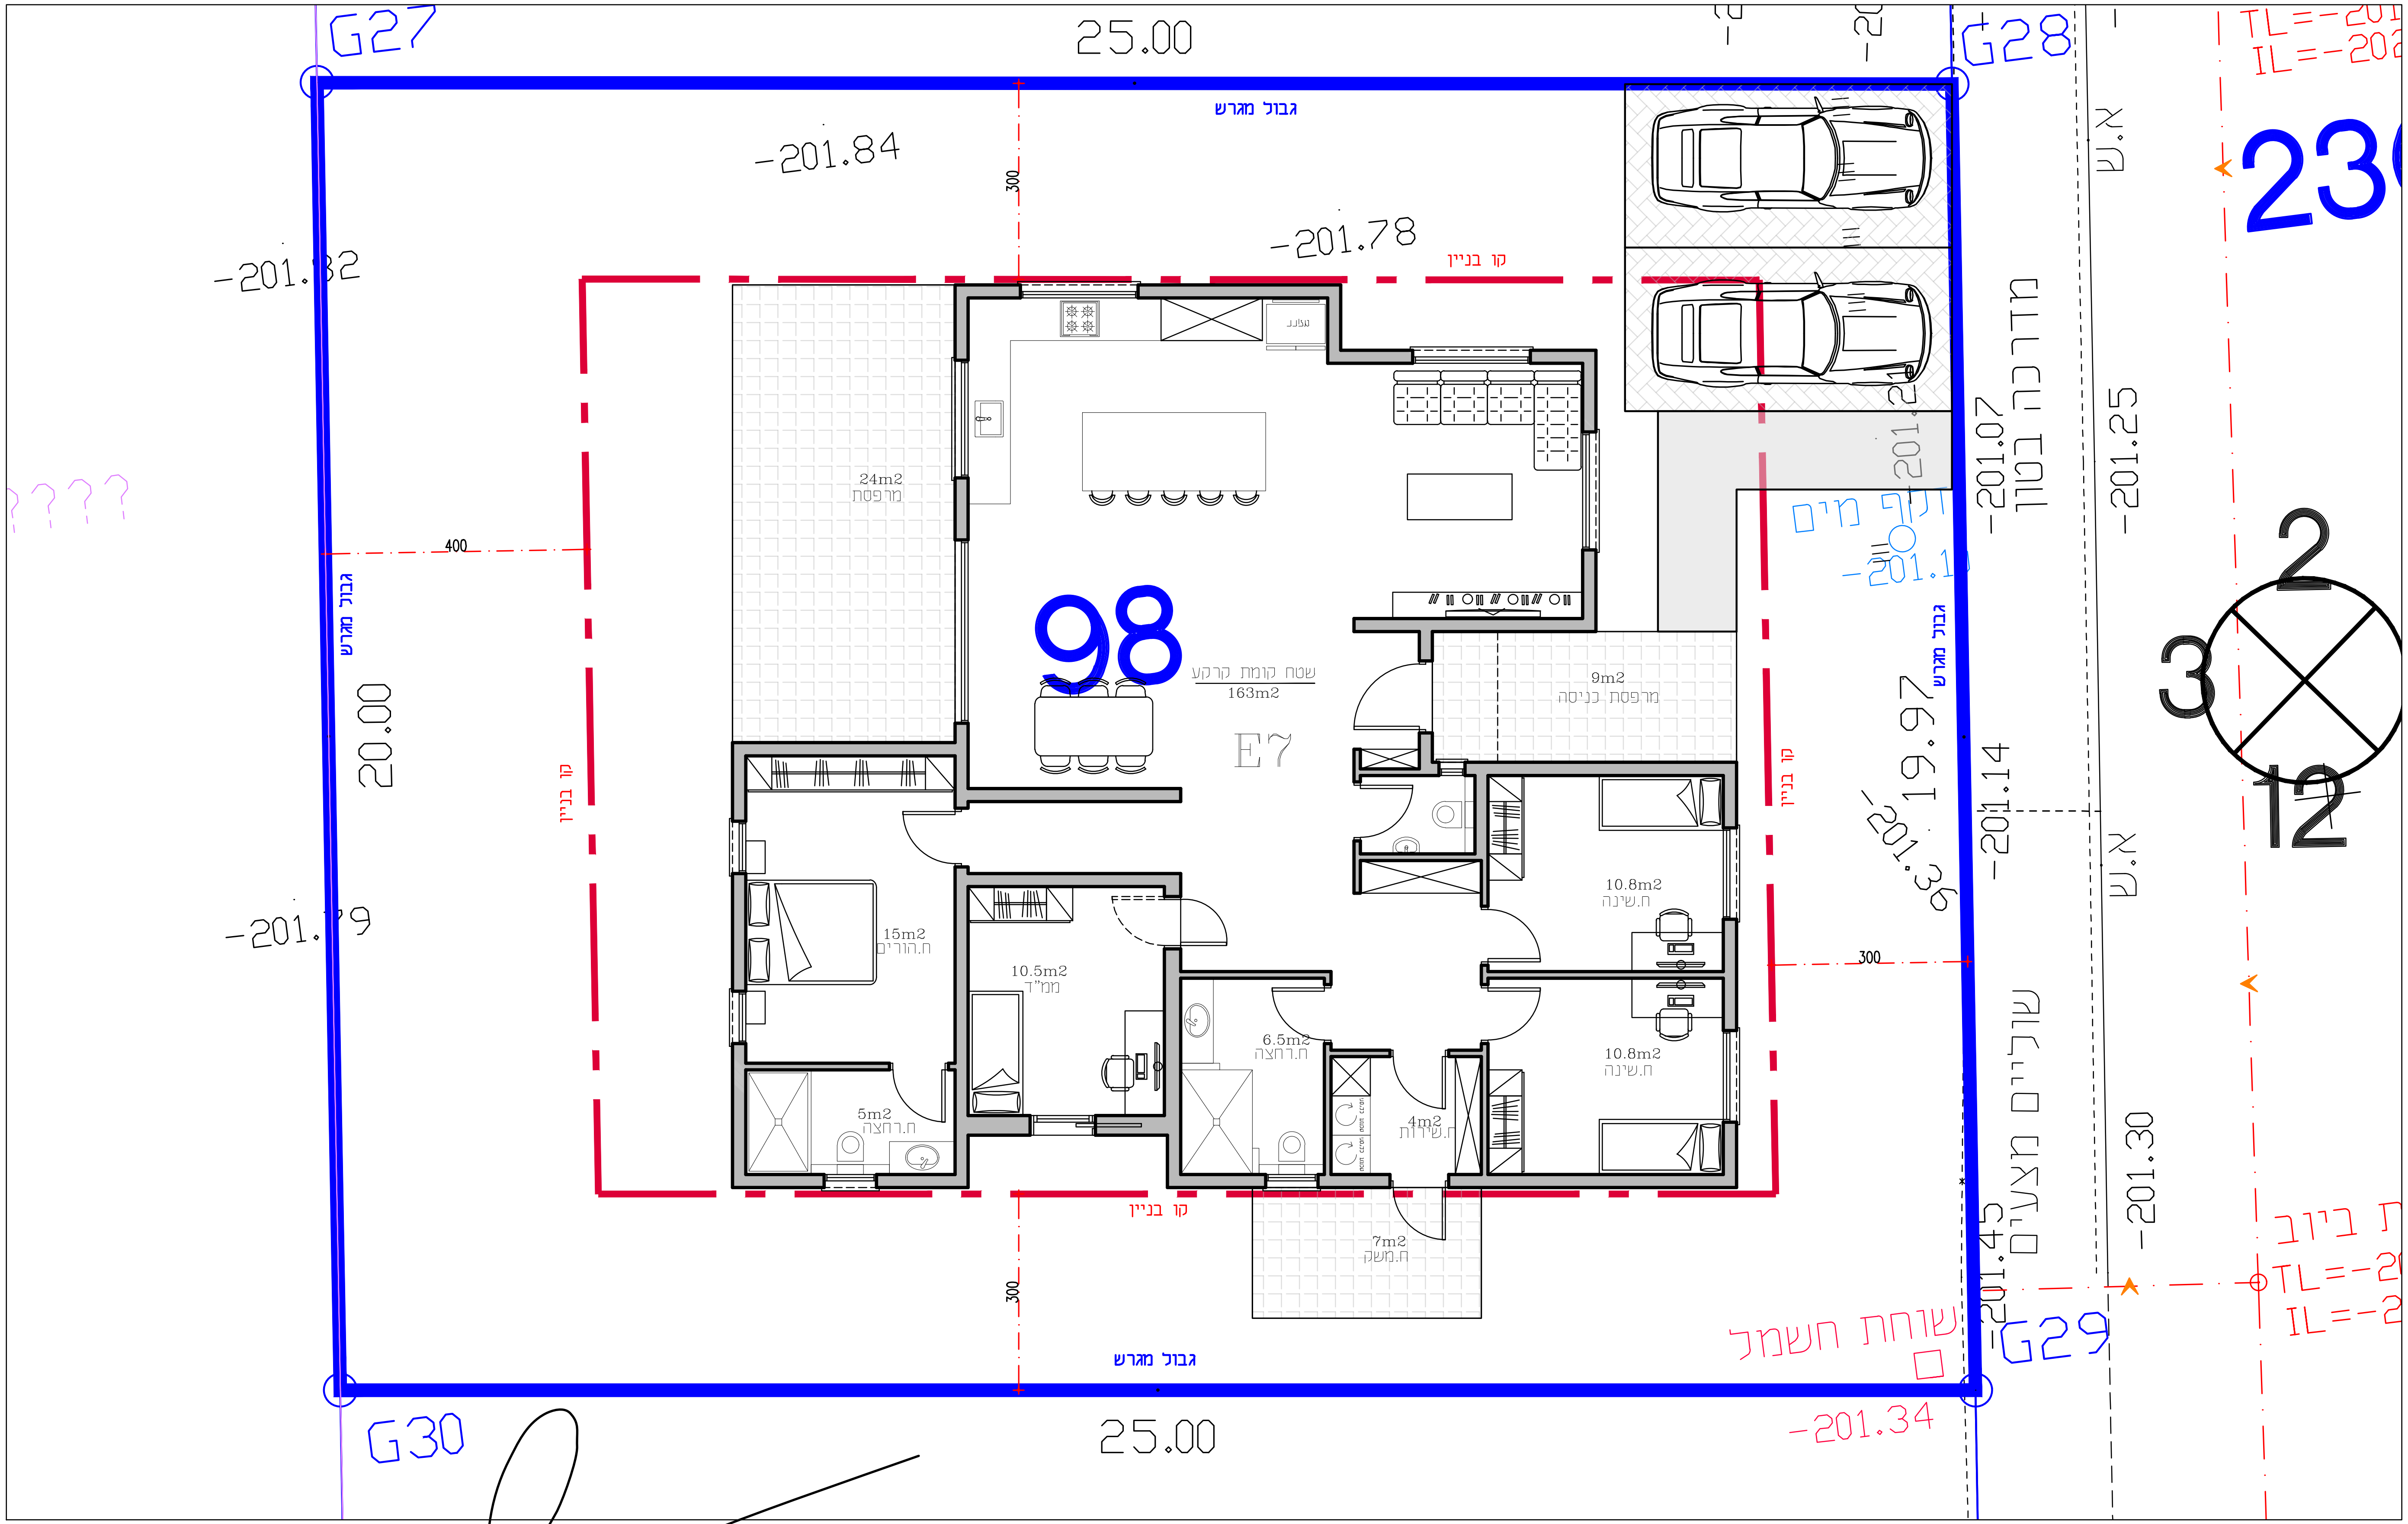
G27
25.00
G28
גבול מגרש
-201.84
-201.78
קו בניין
300
-201.82
????
400
גבול מגרש
20.00
קו בניין
24m2
מרפסת
98
שטח קומת קרקע
163m2
E7
9m2
מרפסת כניסה
15m2
ח.הורים
10.5m2
ממ"ד
6.5m2
ח.רחצה
5m2
ח.רחצה
4m2
ח.שירות
10.8m2
ח.שינה
10.8m2
ח.שינה
7m2
ח.משק
קו בניין
300
גבול מגרש
-201.79
G30
25.00
ברז מים
-201.1
גבול מגרש
קו בניין
19.97
-201.36
-201.14
-201.07
מדרכה בטון
-201.25
שוליים מצעים
-201.45
-201.30
שוחת חשמל
G29
-201.34
א.ש
א.ש
2
3
12
TL=-201
IL=-202
TL=-2
IL=-2

משפחת פרידמן
אפיקים 98

תכנית העמדה
לאישור

קנ"מ 1:100
10.11.26

אוהד אבוטבול 052-8463696
חד-נס רמת הגולן 12950
www.ohadarc.com
ohadarc@gmail.com

OA
Ohad Abutbul
Architecture